


Маркировка камня в осях А5-А9

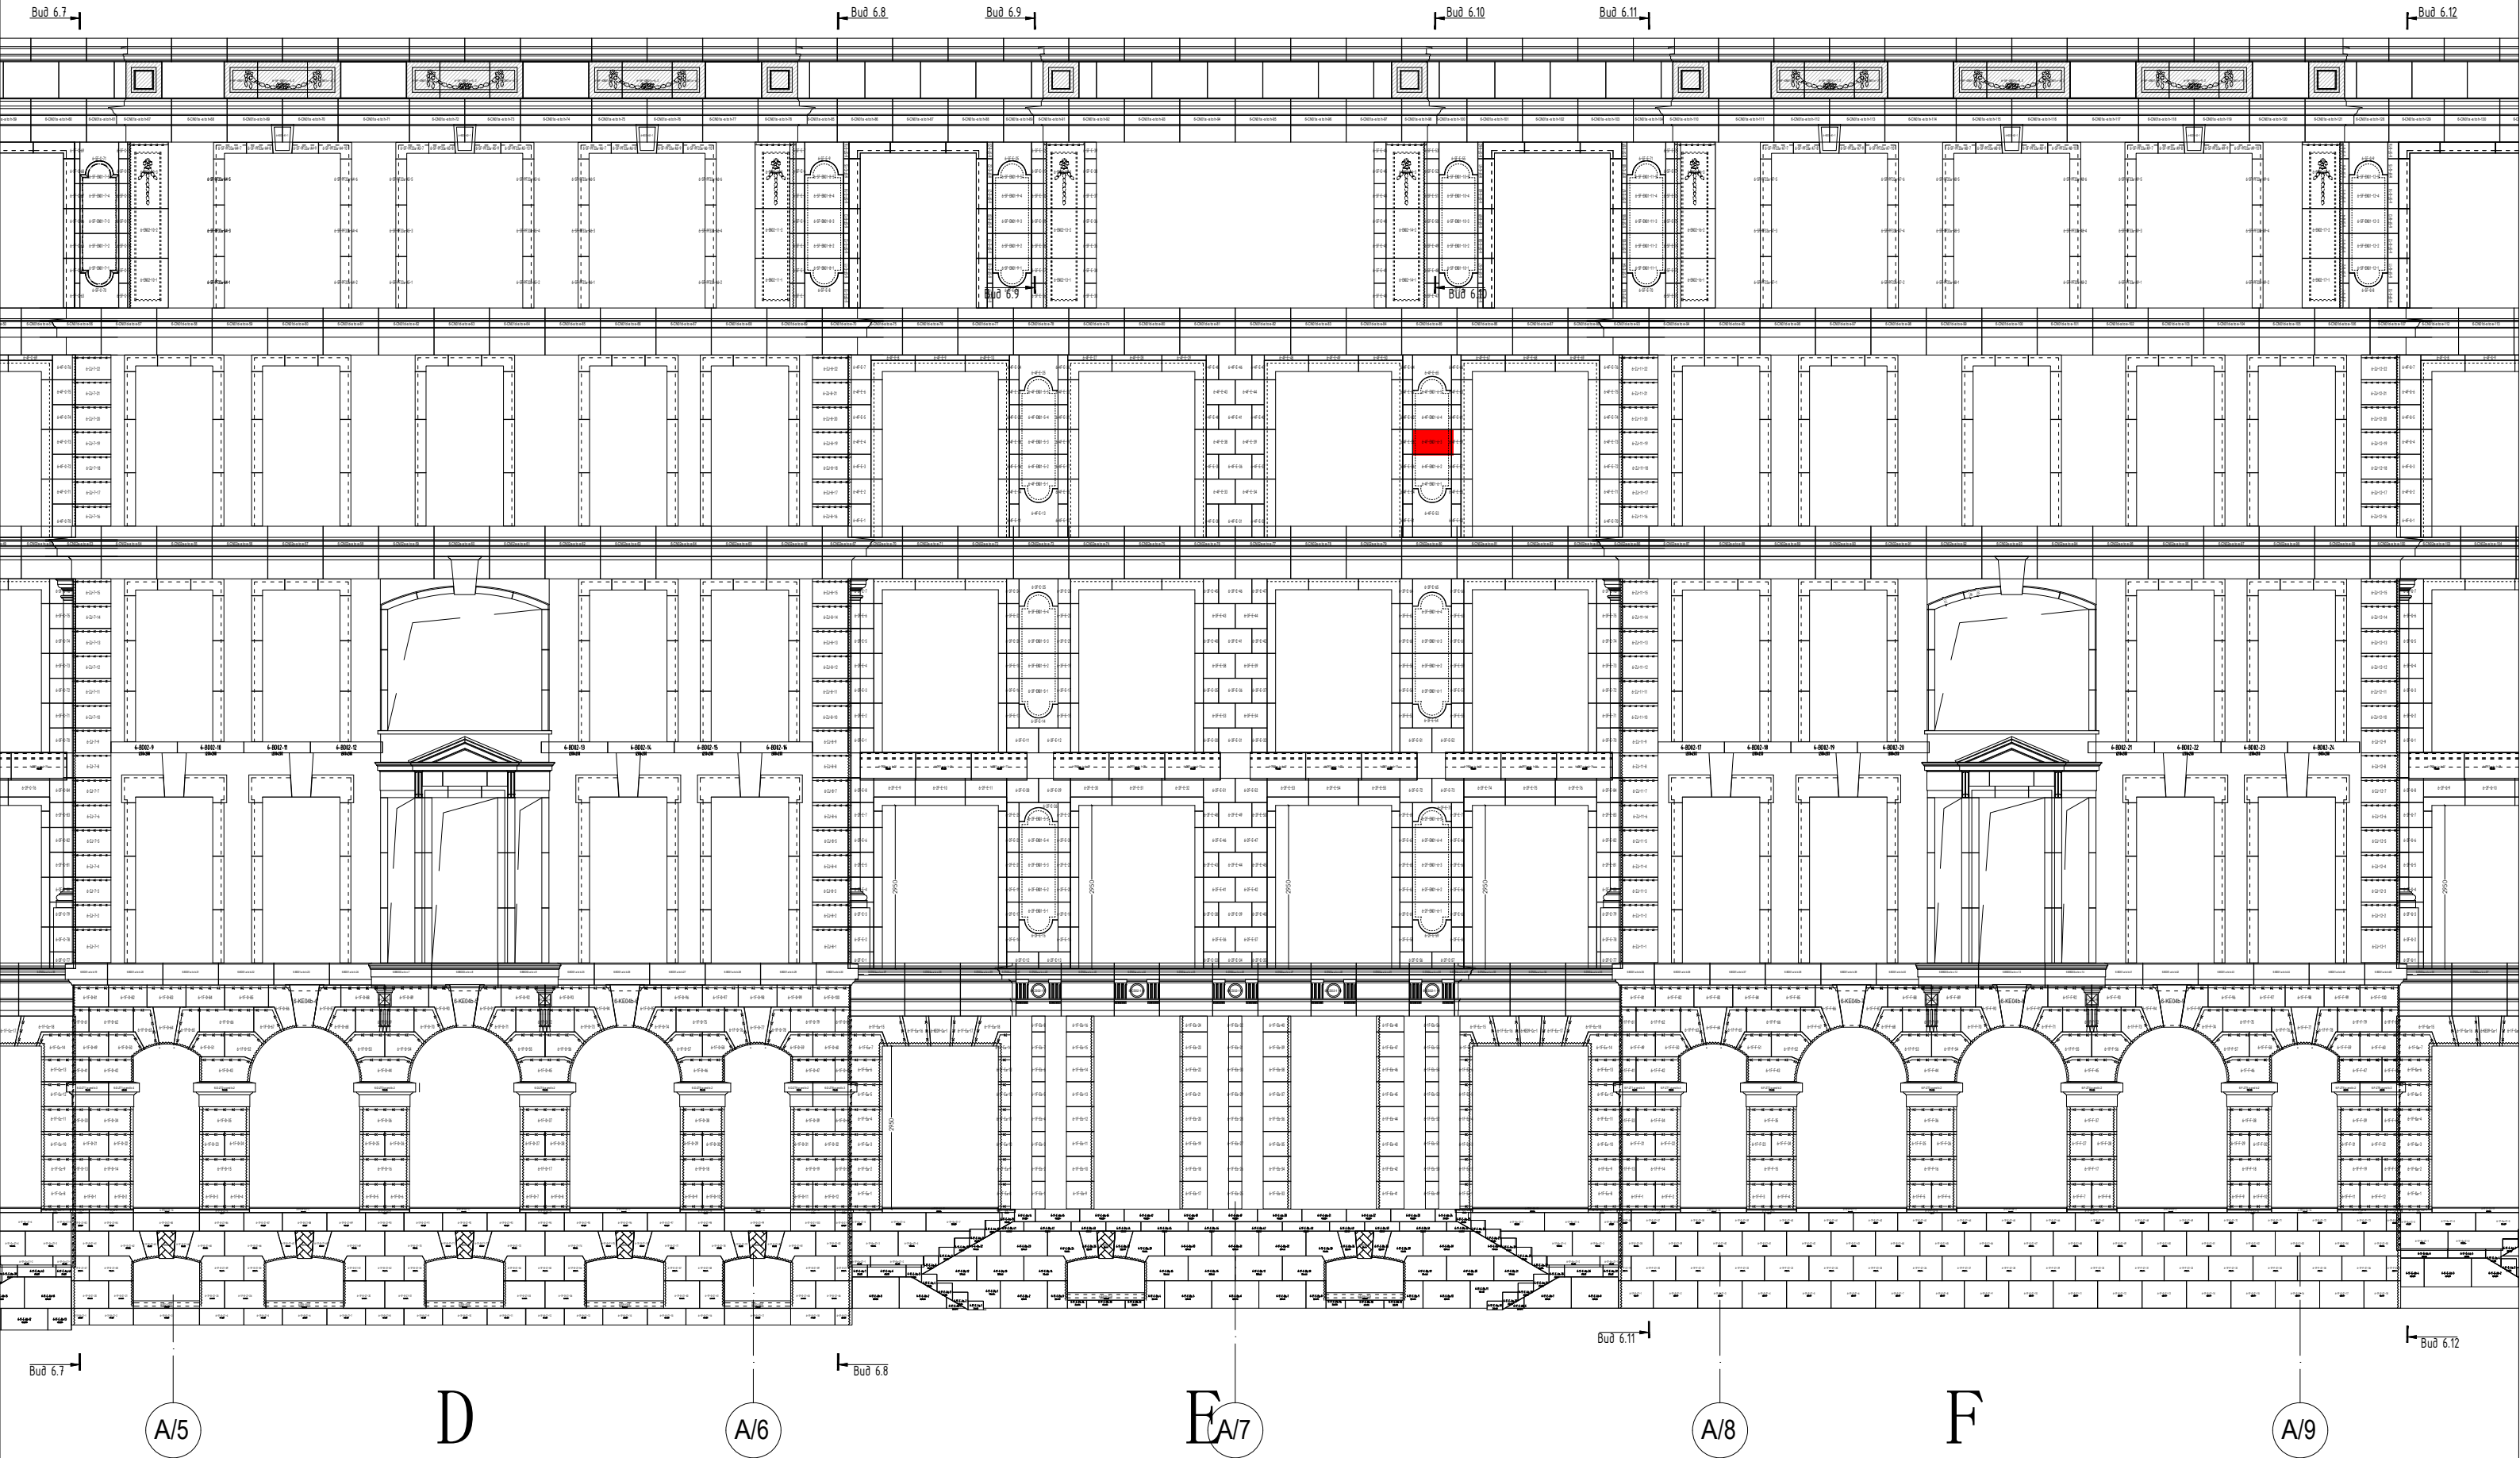

6-4F-EN01-6-3

	工程名称	石材种类	加工单号	下单日期	交货日期	制单人	图号
	6号墙DEF正立面墙身部分						P367